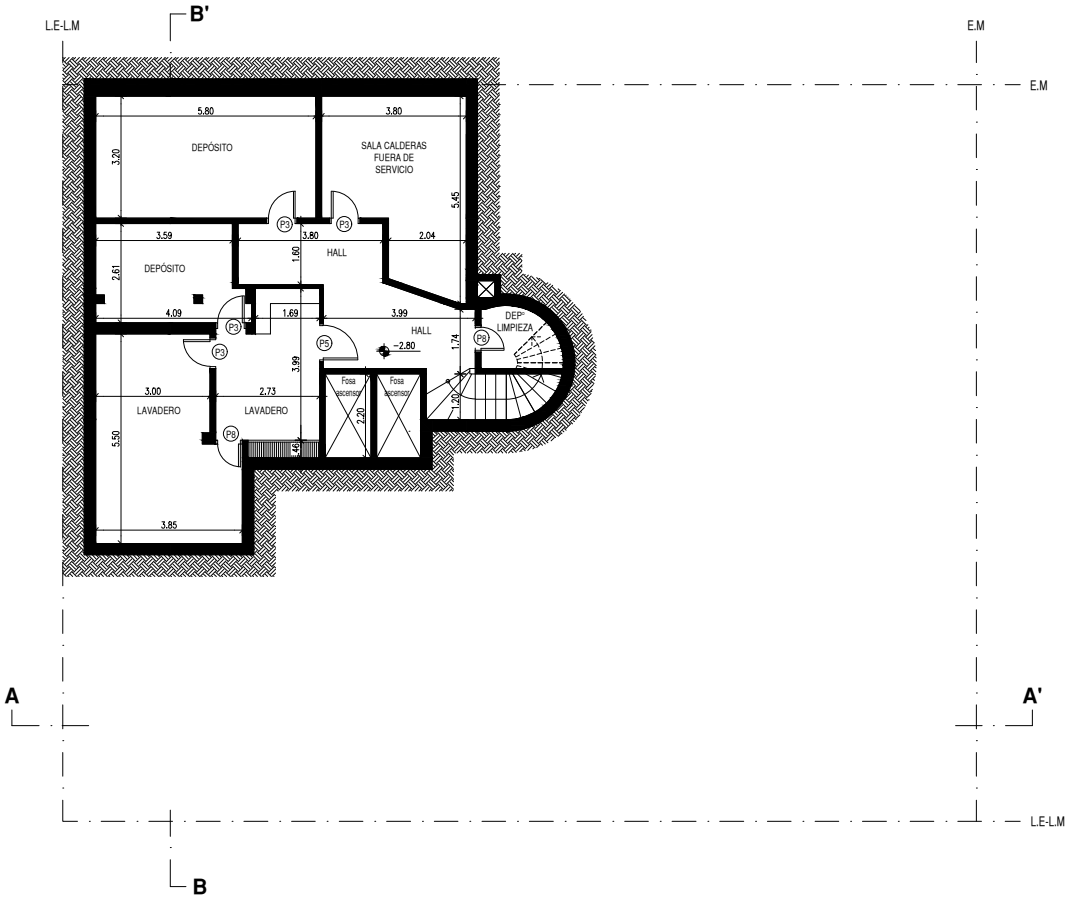


## PLANTA SUBSUELO

ESCALA: 1:100

**PLANILLA SUPERFICIES**

| PLANTA PISOS | SUPERFICIE/M2 |
|---|---|
| PLANTA SUBSUELO | 121.23M2 |
| PLANTA BAJA | 421.72M2 |
| PLANTA 1° PISO | 393.79M2 |
| PLANTA 2° PISO | 406.80M2 |
| PLANTA 3° PISO | 372.36M2 |
| PLANTA 4° PISO | 359.28M2 |
| PLANTA 5° PISO | 359.28M2 |
| PLANTA 6° PISO | 359.45M2 |
| PLANTA 7° PISO | 188.91M2 |
| SUP. CUBIERTA TOTAL | 2982.84M2 |

**PLANILLA DE ABERTURAS**

| TIPO | CANT | DIMENSION | | AREAS | | OBSERVACIÓN |
|---|---|---|---|---|---|---|
| | | ANCHO | ALTO | I° | V° | |
| P1 | 1 | 1.50 | 2.50 | 0.49 | 0.24 | DE ABRIR |
| P2 | 1 | 1.60 | 2.07 | ---- | ---- | DE ABRIR |
| P3 | 58 | 0.80 | 2.00 | ---- | ---- | DE ABRIR |
| P4 | 1 | 0.90 | 2.00 | ---- | ---- | VAIVÉN |
| P5 | 86 | 0.90 | 2.00 | ---- | ---- | DE ABRIR |
| P6 | 3 | 1.40 | 2.00 | ---- | ---- | VAIVÉN |
| P7 | 4 | 1.00 | 2.00 | ---- | ---- | DE ABRIR |
| P8 | 59 | 0.70 | 2.00 | ---- | ---- | DE ABRIR |
| P9 | 1 | 1.16 | 2.00 | ---- | ---- | DE ABRIR |
| P10 | 1 | 0.70 | 2.00 | ---- | ---- | CORREDIZA |
| P11 | 1 | 1.20 | 2.00 | ---- | ---- | DE ABRIR |
| P12 | 8 | 1.30 | 2.00 | ---- | ---- | DE ABRIR |
| P13 | 4 | 0.90 | 2.00 | ---- | ---- | CORREDIZA |
| P14 | 2 | 1.80 | 2.00 | ---- | ---- | DE ABRIR |
| P15 | 2 | 1.75 | 2.00 | ---- | ---- | VAIVÉN |
| P16 | 1 | 1.60 | 2.00 | ---- | ---- | DE ABRIR |
| V1 | 105 | 1.20 | 1.20 | 1.44 | 1.44 | DE ABRIR |
| V2 | 2 | 1.60 | 0.37 | 0.59 | ---- | VIDRIO FIJO |
| V3 | 2 | 0.32 | 2.50 | ---- | ---- | VIDRIO FIJO |
| V4 | 1 | 1.98 | 1.00 | ---- | ---- | VIDRIO FIJO |
| V5 | 1 | 1.20 | 1.20 | 1.44 | 0.72 | CORREDIZA |
| V6 | 2 | 0.85 | 1.00 | 0.85 | 0.85 | DE ABRIR |
| V7 | 3 | 2.40 | 1.20 | 1.08 | 1.08 | CORREDIZA |
| V8 | 13 | 0.90 | 1.50 | 1.35 | 1.35 | DE ABRIR |
| V9 | 17 | 1.40 | 1.20 | 1.68 | 1.68 | DE ABRIR |
| V10 | 5 | 1.90 | 1.50 | 2.85 | 2.85 | DE ABRIR |
| V11 | 7 | 0.90 | 1.20 | 1.08 | 1.08 | DE ABRIR |
| V12 | 1 | 3.00 | 1.50 | 4.50 | 2.25 | BANDEROLA |
| V13 | 3 | 0.50 | 0.35 | 0.18 | 0.09 | BANDEROLA |

# CLINICA PRIVADA : "CHUTRO"

| CIRC. | SECC. | MZA. | PARC. |
|---|---|---|---|
| 04 | 02 | 042 | 030 |

RAZON SOCIAL : CLINICA CHUTRO S.R.L.

CALLE: AV.COLON N° 788 - BARRIO: CENTRO - CORDOBA CAPITAL

CROQUIS DE UBICACIÓN

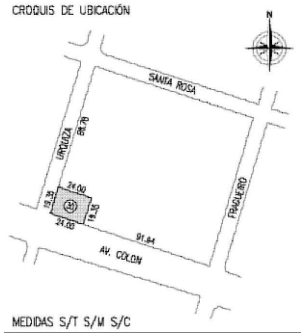


MEDIDAS S/T S/M S/C

TITULAR : BUSTOS RODRIGO

TRANCRIPCION Y RELEVAMIENTO ACTUALIZADO

Gastón Sentagne
ARQUITECTO
M.P. 6723

ARQ. GASTON SENTAGNE
M.P : 1-6723

SUP.DE TERRENO S/T S/C S/M : 464.40

SUP.DE CUB. DE USO ACTIVIDAD: 2982.84

LEGAJO N°

OBSERVACIONES

CONTENIDO : PLANO SUB SUELO

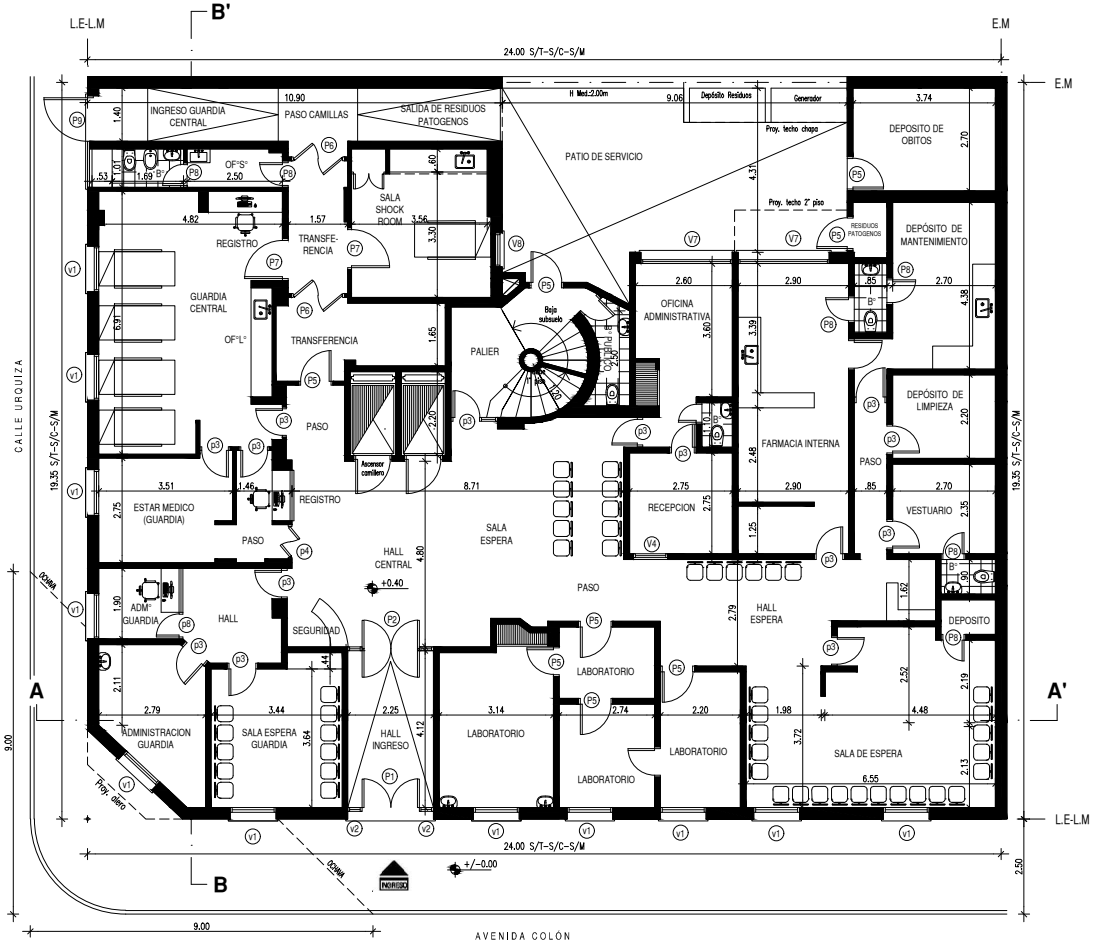


# PLANTA BAJA

ESCALA: 1:100

**PLANILLA SUPERFICIES**

| PLANTA PISOS | SUPERFICIE/M2 |
|---|---|
| PLANTA SUBSUELO | 121.23M2 |
| PLANTA BAJA | 421.72M2 |
| PLANTA 1° PISO | 393.79M2 |
| PLANTA 2° PISO | 406.80M2 |
| PLANTA 3° PISO | 372.36M2 |
| PLANTA 4° PISO | 359.28M2 |
| PLANTA 5° PISO | 359.28M2 |
| PLANTA 6° PISO | 359.45M2 |
| PLANTA 7° PISO | 188.91M2 |
| SUP. CUBIERTA TOTAL | 2982.84M2 |

**PLANILLA DE ABERTURAS**

| TIPO | CANT | DIMENSION | | AREAS | | OBSERVACIÓN |
|---|---|---|---|---|---|---|
| | | ANCHO | ALTO | I° | V° | |
| P1 | 1 | 1.50 | 2.50 | 0.49 | 0.24 | DE ABRIR |
| P2 | 1 | 1.60 | 2.07 | ---- | ---- | DE ABRIR |
| P3 | 58 | 0.80 | 2.00 | ---- | ---- | DE ABRIR |
| P4 | 1 | 0.90 | 2.00 | ---- | ---- | VAIVÉN |
| P5 | 86 | 0.90 | 2.00 | ---- | ---- | DE ABRIR |
| P6 | 3 | 1.40 | 2.00 | ---- | ---- | VAIVÉN |
| P7 | 4 | 1.00 | 2.00 | ---- | ---- | DE ABRIR |
| P8 | 59 | 0.70 | 2.00 | ---- | ---- | DE ABRIR |
| P9 | 1 | 1.16 | 2.00 | ---- | ---- | DE ABRIR |
| P10 | 1 | 0.70 | 2.00 | ---- | ---- | CORREDIZA |
| P11 | 1 | 1.20 | 2.00 | ---- | ---- | DE ABRIR |
| P12 | 8 | 1.30 | 2.00 | ---- | ---- | DE ABRIR |
| P13 | 4 | 0.90 | 2.00 | ---- | ---- | CORREDIZA |
| P14 | 2 | 1.80 | 2.00 | ---- | ---- | DE ABRIR |
| P15 | 2 | 1.75 | 2.00 | ---- | ---- | VAIVÉN |
| P16 | 1 | 1.60 | 2.00 | ---- | ---- | DE ABRIR |
| V1 | 105 | 1.20 | 1.20 | 1.44 | 1.44 | DE ABRIR |
| V2 | 2 | 1.60 | 0.37 | 0.59 | ---- | VIDRIO FIJO |
| V3 | 2 | 0.32 | 2.50 | ---- | ---- | VIDRIO FIJO |
| V4 | 1 | 1.98 | 1.00 | ---- | ---- | VIDRIO FIJO |
| V5 | 1 | 1.20 | 1.20 | 1.44 | 0.72 | CORREDIZA |
| V6 | 2 | 0.85 | 1.00 | 0.85 | 0.85 | DE ABRIR |
| V7 | 3 | 2.40 | 1.20 | 1.08 | 1.08 | CORREDIZA |
| V8 | 13 | 0.90 | 1.50 | 1.35 | 1.35 | DE ABRIR |
| V9 | 17 | 1.40 | 1.20 | 1.68 | 1.68 | DE ABRIR |
| V10 | 5 | 1.90 | 1.50 | 2.85 | 2.85 | DE ABRIR |
| V11 | 7 | 0.90 | 1.20 | 1.08 | 1.08 | DE ABRIR |
| V12 | 1 | 3.00 | 1.50 | 4.50 | 2.25 | BANDEROLA |
| V13 | 3 | 0.50 | 0.35 | 0.18 | 0.09 | BANDEROLA |

# CLINICA PRIVADA : "CHUTRO"

| CIRC. | SECC. | MZA. | PARC. |
|---|---|---|---|
| 04 | 02 | 042 | 030 |

RAZON SOCIAL : CLINICA CHUTRO S.R.L.

CALLE: AV.COLON N° 788 - BARRIO: CENTRO - CORDOBA CAPITAL

CROQUIS DE UBICACIÓN

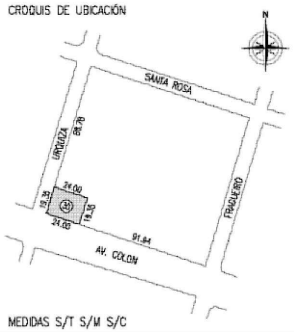


MEDIDAS S/T S/M S/C

TITULAR : BUSTOS RODRIGO

TRANSCRIPCION Y RELEVAMIENTO ACTUALIZADO

Gastón Sentagne
ARQUITECTO
M.P. 6723

ARQ. GASTON SENTAGNE
M.P : 1-6723

SUP.DE TERRENO S/T S/C S/M : 464.40

SUP.DE CUB. DE USO ACTIVIDAD: 2982.84

LEGAJO N°

OBSERVACIONES

CONTENIDO : PLANTA BAJA

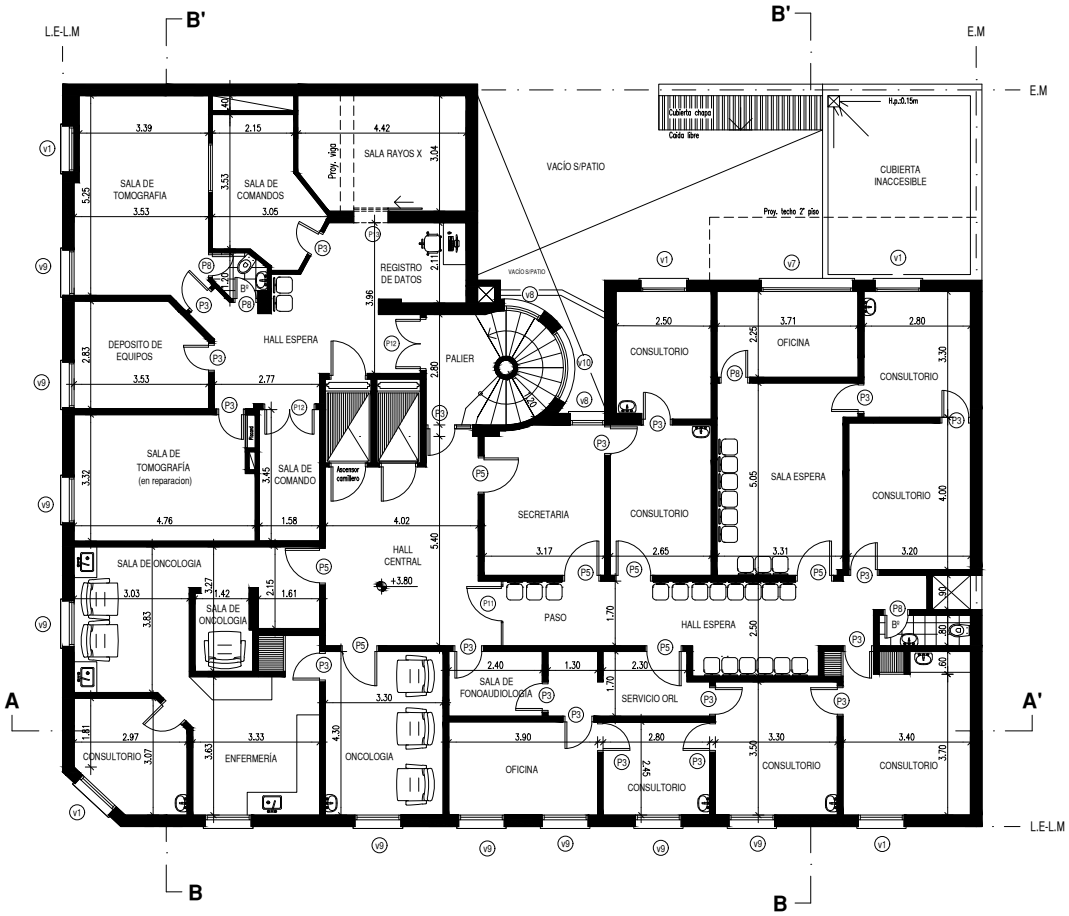


## PLANTA 1° PISO

ESCALA: 1:100

**PLANILLA SUPERFICIES**

| PLANTA PISOS | SUPERFICIE/M2 |
|---|---|
| PLANTA SUBSUELO | 121.23M2 |
| PLANTA BAJA | 421.72M2 |
| PLANTA 1° PISO | 393.79M2 |
| PLANTA 2° PISO | 406.80M2 |
| PLANTA 3° PISO | 372.36M2 |
| PLANTA 4° PISO | 359.28M2 |
| PLANTA 5° PISO | 359.28M2 |
| PLANTA 6° PISO | 359.45M2 |
| PLANTA 7° PISO | 188.91M2 |
| SUP. CUBIERTA TOTAL | 2982.84M2 |

**PLANILLA DE ABERTURAS**

| TIPO | CANT | DIMENSION | | AREAS | | OBSERVACIÓN |
|---|---|---|---|---|---|---|
| | | ANCHO | ALTO | I° | V° | |
| P1 | 1 | 1.50 | 2.50 | 0.49 | 0.24 | DE ABRIR |
| P2 | 1 | 1.60 | 2.07 | ---- | ---- | DE ABRIR |
| P3 | 58 | 0.80 | 2.00 | ---- | ---- | DE ABRIR |
| P4 | 1 | 0.90 | 2.00 | ---- | ---- | VAIVÉN |
| P5 | 86 | 0.90 | 2.00 | ---- | ---- | DE ABRIR |
| P6 | 3 | 1.40 | 2.00 | ---- | ---- | VAIVÉN |
| P7 | 4 | 1.00 | 2.00 | ---- | ---- | DE ABRIR |
| P8 | 59 | 0.70 | 2.00 | ---- | ---- | DE ABRIR |
| P9 | 1 | 1.16 | 2.00 | ---- | ---- | DE ABRIR |
| P10 | 1 | 0.70 | 2.00 | ---- | ---- | CORREDIZA |
| P11 | 1 | 1.20 | 2.00 | ---- | ---- | DE ABRIR |
| P12 | 8 | 1.30 | 2.00 | ---- | ---- | DE ABRIR |
| P13 | 4 | 0.90 | 2.00 | ---- | ---- | CORREDIZA |
| P14 | 2 | 1.80 | 2.00 | ---- | ---- | DE ABRIR |
| P15 | 2 | 1.75 | 2.00 | ---- | ---- | VAIVÉN |
| P16 | 1 | 1.60 | 2.00 | ---- | ---- | DE ABRIR |
| V1 | 105 | 1.20 | 1.20 | 1.44 | 1.44 | DE ABRIR |
| V2 | 2 | 1.60 | 0.37 | 0.59 | ---- | VIDRIO FIJO |
| V3 | 2 | 0.32 | 2.50 | ---- | ---- | VIDRIO FIJO |
| V4 | 1 | 1.98 | 1.00 | ---- | ---- | VIDRIO FIJO |
| V5 | 1 | 1.20 | 1.20 | 1.44 | 0.72 | CORREDIZA |
| V6 | 2 | 0.85 | 1.00 | 0.85 | 0.85 | DE ABRIR |
| V7 | 3 | 2.40 | 1.20 | 1.08 | 1.08 | CORREDIZA |
| V8 | 13 | 0.90 | 1.50 | 1.35 | 1.35 | DE ABRIR |
| V9 | 17 | 1.40 | 1.20 | 1.68 | 1.68 | DE ABRIR |
| V10 | 5 | 1.90 | 1.50 | 2.85 | 2.85 | DE ABRIR |
| V11 | 7 | 0.90 | 1.20 | 1.08 | 1.08 | DE ABRIR |
| V12 | 1 | 3.00 | 1.50 | 4.50 | 2.25 | BANDEROLA |
| V13 | 3 | 0.50 | 0.35 | 0.18 | 0.09 | BANDEROLA |

# CLINICA PRIVADA : "CHUTRO"

| CIRC. | SECC. | MZA. | PARC. |
|---|---|---|---|
| 04 | 02 | 042 | 030 |

RAZON SOCIAL : CLINICA CHUTRO S.R.L.

CALLE: AV.COLON N° 788 - BARRIO: CENTRO - CORDOBA CAPITAL

CROQUIS DE UBICACIÓN

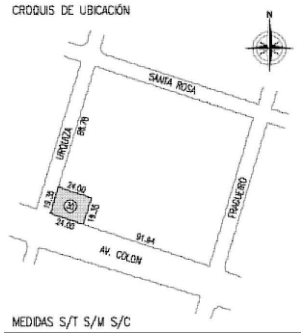


MEDIDAS S/T S/M S/C

TITULAR : BUSTOS RODRIGO

TRANSCRIPCION Y RELEVAMIENTO ACTUALIZADO

Gastón Sentagne
ARQUITECTO
M.P. 6723

ARQ. GASTON SENTAGNE
M.P : 1-6723

SUP.DE TERRENO S/T S/C S/M : 464.40

SUP.DE CUB. DE USO ACTIVIDAD: 2982.84

LEGAJO N°

OBSERVACIONES

CONTENIDO : PLANTA PRIMER PISO

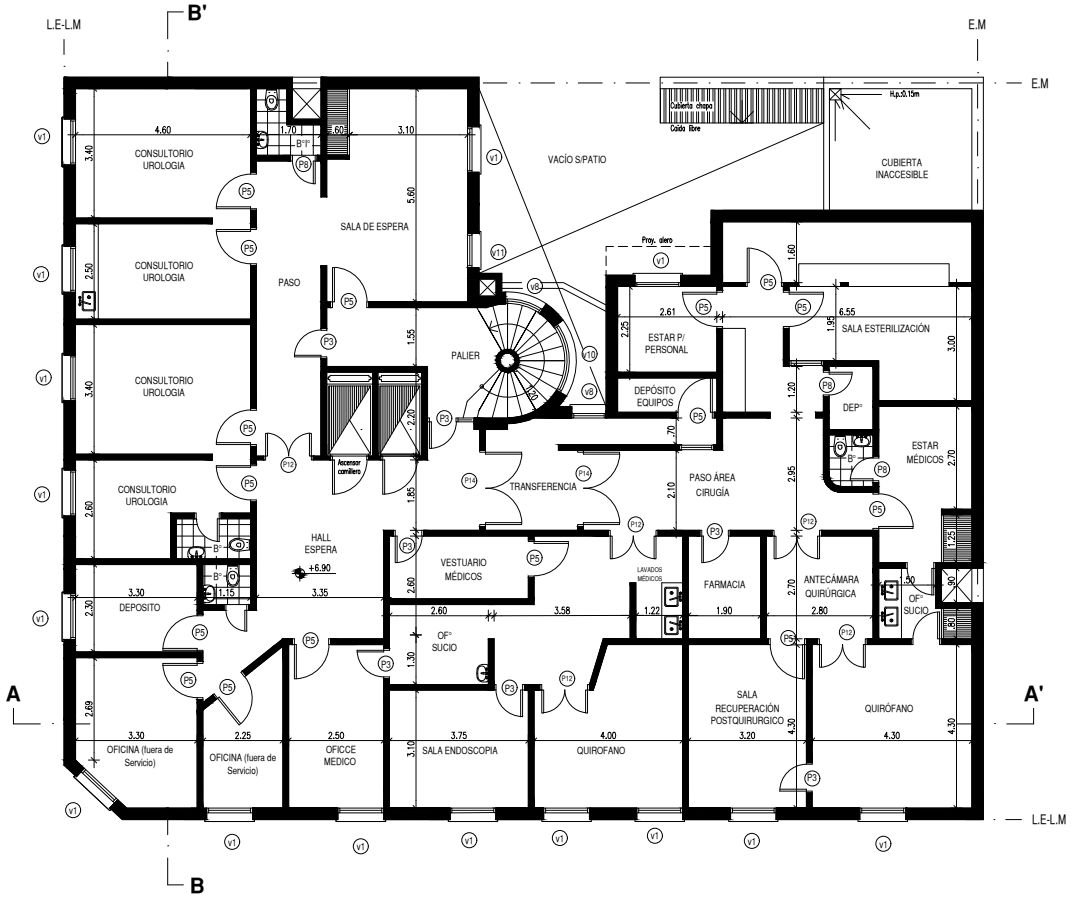


# PLANTA 2° PISO

ESCALA: 1:100

**PLANILLA SUPERFICIES**

| PLANTA PISOS | SUPERFICIE/M2 |
|---|---|
| PLANTA SUBSUELO | 121.23M2 |
| PLANTA BAJA | 421.72M2 |
| PLANTA 1° PISO | 393.79M2 |
| PLANTA 2° PISO | 406.80M2 |
| PLANTA 3° PISO | 372.36M2 |
| PLANTA 4° PISO | 359.28M2 |
| PLANTA 5° PISO | 359.28M2 |
| PLANTA 6° PISO | 359.45M2 |
| PLANTA 7° PISO | 188.91M2 |
| SUP. CUBIERTA TOTAL | 2982.84M2 |

**PLANILLA DE ABERTURAS**

| TIPO | CANT | DIMENSION | | AREAS | | OBSERVACIÓN |
|---|---|---|---|---|---|---|
| | | ANCHO | ALTO | I° | V° | |
| P1 | 1 | 1.50 | 2.50 | 0.49 | 0.24 | DE ABRIR |
| P2 | 1 | 1.60 | 2.07 | ---- | ---- | DE ABRIR |
| P3 | 58 | 0.80 | 2.00 | ---- | ---- | DE ABRIR |
| P4 | 1 | 0.90 | 2.00 | ---- | ---- | VAIVÉN |
| P5 | 86 | 0.90 | 2.00 | ---- | ---- | DE ABRIR |
| P6 | 3 | 1.40 | 2.00 | ---- | ---- | VAIVÉN |
| P7 | 4 | 1.00 | 2.00 | ---- | ---- | DE ABRIR |
| P8 | 59 | 0.70 | 2.00 | ---- | ---- | DE ABRIR |
| P9 | 1 | 1.16 | 2.00 | ---- | ---- | DE ABRIR |
| P10 | 1 | 0.70 | 2.00 | ---- | ---- | CORREDIZA |
| P11 | 1 | 1.20 | 2.00 | ---- | ---- | DE ABRIR |
| P12 | 8 | 1.30 | 2.00 | ---- | ---- | DE ABRIR |
| P13 | 4 | 0.90 | 2.00 | ---- | ---- | CORREDIZA |
| P14 | 2 | 1.80 | 2.00 | ---- | ---- | DE ABRIR |
| P15 | 2 | 1.75 | 2.00 | ---- | ---- | VAIVÉN |
| P16 | 1 | 1.60 | 2.00 | ---- | ---- | DE ABRIR |
| V1 | 105 | 1.20 | 1.20 | 1.44 | 1.44 | DE ABRIR |
| V2 | 2 | 1.60 | 0.37 | 0.59 | ---- | VIDRIO FIJO |
| V3 | 2 | 0.32 | 2.50 | ---- | ---- | VIDRIO FIJO |
| V4 | 1 | 1.98 | 1.00 | ---- | ---- | VIDRIO FIJO |
| V5 | 1 | 1.20 | 1.20 | 1.44 | 0.72 | CORREDIZA |
| V6 | 2 | 0.85 | 1.00 | 0.85 | 0.85 | DE ABRIR |
| V7 | 3 | 2.40 | 1.20 | 1.08 | 1.08 | CORREDIZA |
| V8 | 13 | 0.90 | 1.50 | 1.35 | 1.35 | DE ABRIR |
| V9 | 17 | 1.40 | 1.20 | 1.68 | 1.68 | DE ABRIR |
| V10 | 5 | 1.90 | 1.50 | 2.85 | 2.85 | DE ABRIR |
| V11 | 7 | 0.90 | 1.20 | 1.08 | 1.08 | DE ABRIR |
| V12 | 1 | 3.00 | 1.50 | 4.50 | 2.25 | BANDEROLA |
| V13 | 3 | 0.50 | 0.35 | 0.18 | 0.09 | BANDEROLA |

## CLINICA PRIVADA : "CHUTRO"

| CIRC. | SECC. | MZA. | PARC. |
|---|---|---|---|
| 04 | 02 | 042 | 030 |

RAZON SOCIAL : CLINICA CHUTRO S.R.L.

CALLE: AV.COLON N° 788 - BARRIO: CENTRO - CORDOBA CAPITAL

CROQUIS DE UBICACIÓN

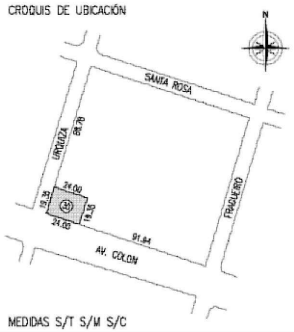


TITULAR : BUSTOS RODRIGO

TRANSCRIPCION Y RELEVAMIENTO ACTUALIZADO

Gastón Sentagne
ARQUITECTO
M.P. 6723

ARQ. GASTON SENTAGNE
M.P : 1-6723

SUP.DE TERRENO S/T S/C S/M : 464.40

SUP.DE CUB. DE USO ACTIVIDAD: 2982.84

LEGAJO N°

OBSERVACIONES

CONTENIDO : PLANTA SEGUNDO PISO

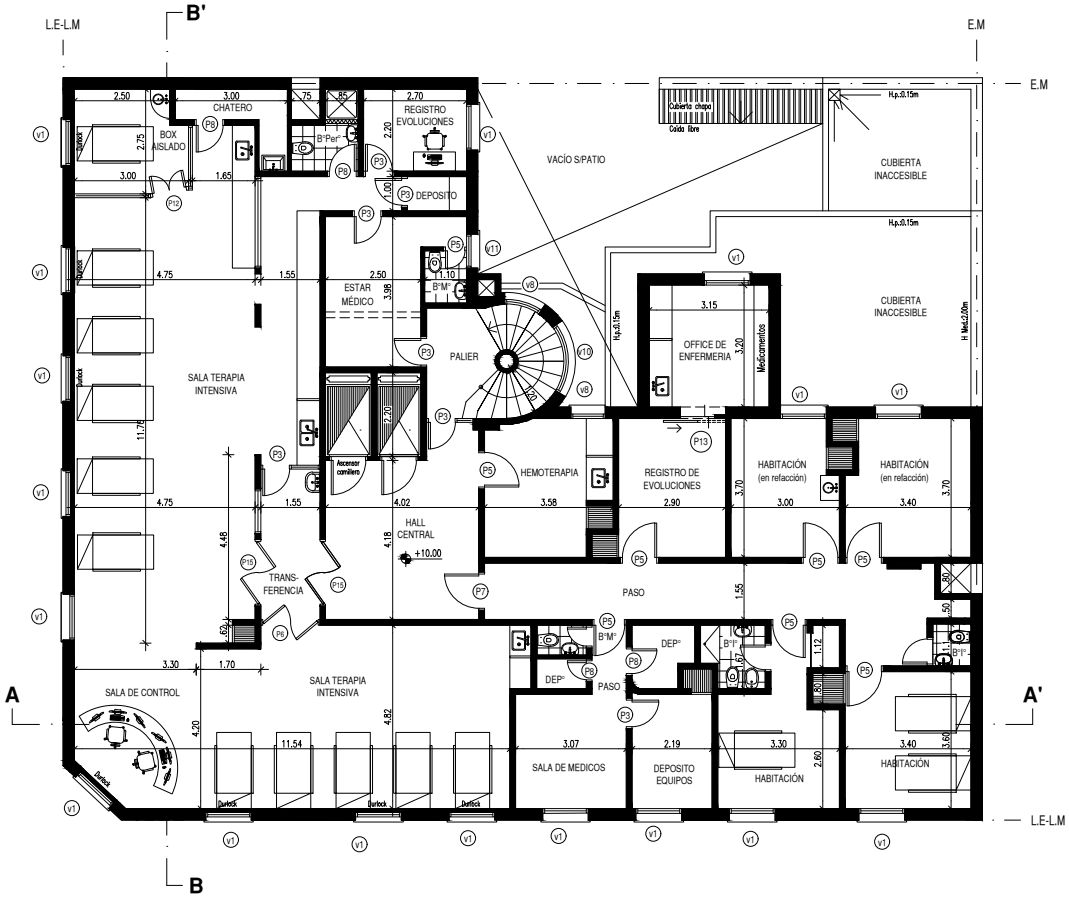


# PLANTA 3° PISO

ESCALA: 1:100

**PLANILLA SUPERFICIES**

| PLANTA PISOS | SUPERFICIE/M2 |
|---|---|
| PLANTA SUBSUELO | 121.23M2 |
| PLANTA BAJA | 421.72M2 |
| PLANTA 1° PISO | 393.79M2 |
| PLANTA 2° PISO | 406.80M2 |
| PLANTA 3° PISO | 372.36M2 |
| PLANTA 4° PISO | 359.28M2 |
| PLANTA 5° PISO | 359.28M2 |
| PLANTA 6° PISO | 359.45M2 |
| PLANTA 7° PISO | 188.91M2 |
| SUP. CUBIERTA TOTAL | 2982.84M2 |

**PLANILLA DE ABERTURAS**

| TIPO | CANT | DIMENSION | | AREAS | | OBSERVACIÓN |
|---|---|---|---|---|---|---|
| | | ANCHO | ALTO | I° | V° | |
| P1 | 1 | 1.50 | 2.50 | 0.49 | 0.24 | DE ABRIR |
| P2 | 1 | 1.60 | 2.07 | ---- | ---- | DE ABRIR |
| P3 | 58 | 0.80 | 2.00 | ---- | ---- | DE ABRIR |
| P4 | 1 | 0.90 | 2.00 | ---- | ---- | VAIVÉN |
| P5 | 86 | 0.90 | 2.00 | ---- | ---- | DE ABRIR |
| P6 | 3 | 1.40 | 2.00 | ---- | ---- | VAIVÉN |
| P7 | 4 | 1.00 | 2.00 | ---- | ---- | DE ABRIR |
| P8 | 59 | 0.70 | 2.00 | ---- | ---- | DE ABRIR |
| P9 | 1 | 1.16 | 2.00 | ---- | ---- | DE ABRIR |
| P10 | 1 | 0.70 | 2.00 | ---- | ---- | CORREDIZA |
| P11 | 1 | 1.20 | 2.00 | ---- | ---- | DE ABRIR |
| P12 | 8 | 1.30 | 2.00 | ---- | ---- | DE ABRIR |
| P13 | 4 | 0.90 | 2.00 | ---- | ---- | CORREDIZA |
| P14 | 2 | 1.80 | 2.00 | ---- | ---- | DE ABRIR |
| P15 | 2 | 1.75 | 2.00 | ---- | ---- | VAIVÉN |
| P16 | 1 | 1.60 | 2.00 | ---- | ---- | DE ABRIR |
| V1 | 105 | 1.20 | 1.20 | 1.44 | 1.44 | DE ABRIR |
| V2 | 2 | 1.60 | 0.37 | 0.59 | ---- | VIDRIO FIJO |
| V3 | 2 | 0.32 | 2.50 | ---- | ---- | VIDRIO FIJO |
| V4 | 1 | 1.98 | 1.00 | ---- | ---- | VIDRIO FIJO |
| V5 | 1 | 1.20 | 1.20 | 1.44 | 0.72 | CORREDIZA |
| V6 | 2 | 0.85 | 1.00 | 0.85 | 0.85 | DE ABRIR |
| V7 | 3 | 2.40 | 1.20 | 1.08 | 1.08 | CORREDIZA |
| V8 | 13 | 0.90 | 1.50 | 1.35 | 1.35 | DE ABRIR |
| V9 | 17 | 1.40 | 1.20 | 1.68 | 1.68 | DE ABRIR |
| V10 | 5 | 1.90 | 1.50 | 2.85 | 2.85 | DE ABRIR |
| V11 | 7 | 0.90 | 1.20 | 1.08 | 1.08 | DE ABRIR |
| V12 | 1 | 3.00 | 1.50 | 4.50 | 2.25 | BANDEROLA |
| V13 | 3 | 0.50 | 0.35 | 0.18 | 0.09 | BANDEROLA |

## CLINICA PRIVADA : "CHUTRO"

| CIRC. | SECC. | MZA. | PARC. |
|---|---|---|---|
| 04 | 02 | 042 | 030 |

RAZON SOCIAL : CLINICA CHUTRO S.R.L.

CALLE: AV.COLON N° 788 - BARRIO: CENTRO - CORDOBA CAPITAL

CROQUIS DE UBICACIÓN

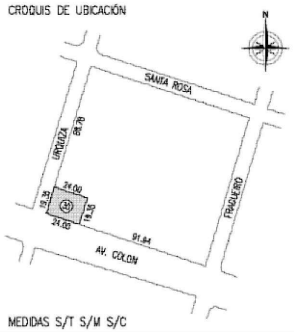


MEDIDAS S/T S/M S/C

TITULAR : BUSTOS RODRIGO

TRANSCRIPCION Y RELEVAMIENTO ACTUALIZADO

Gastón Sentagne
ARQUITECTO
M.P. 6723

ARQ. GASTON SENTAGNE
M.P : 1-6723

SUP.DE TERRENO S/T S/C S/M : 464.40

SUP.DE CUB. DE USO ACTIVIDAD: 2982.84

LEGAJO N°

OBSERVACIONES

CONTENIDO : PLANTA TERCER PISO

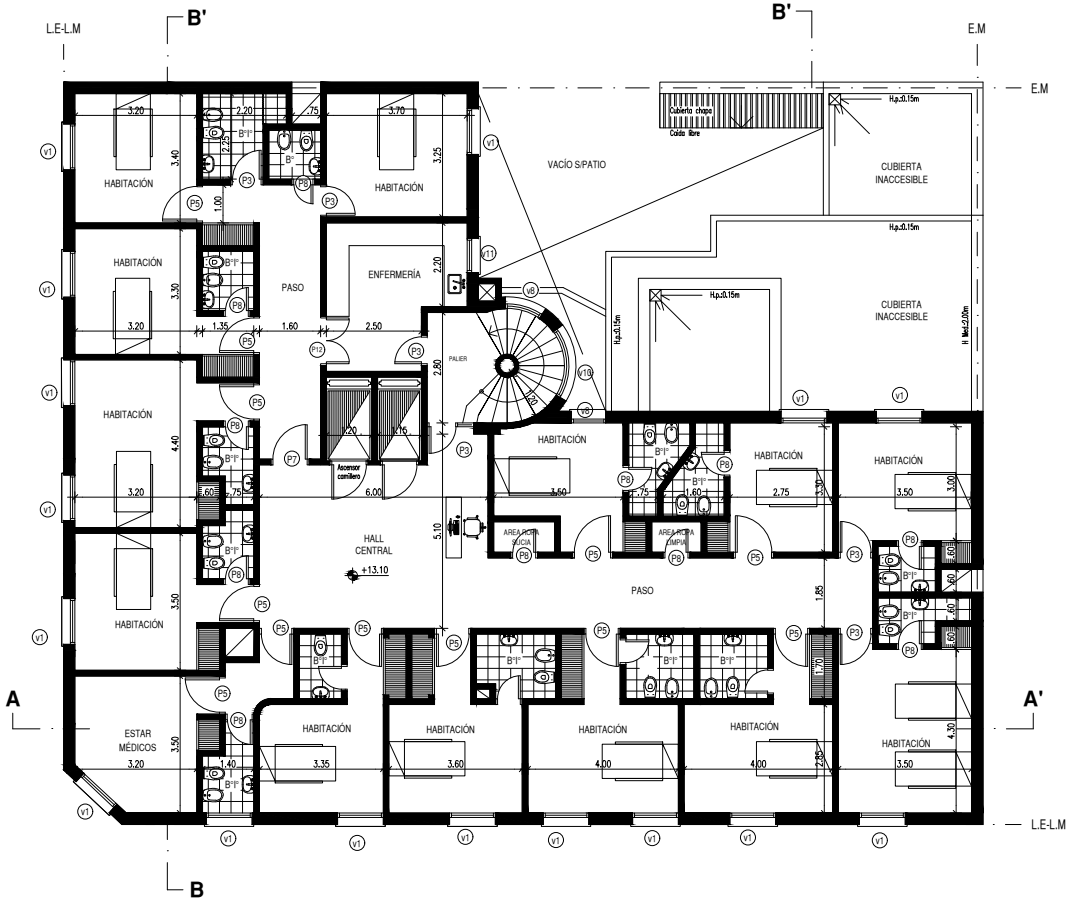


# PLANTA 4° PISO

ESCALA: 1:100

**PLANILLA SUPERFICIES**

| PLANTA PISOS | SUPERFICIE/M2 |
|---|---|
| PLANTA SUBSUELO | 121.23M2 |
| PLANTA BAJA | 421.72M2 |
| PLANTA 1° PISO | 393.79M2 |
| PLANTA 2° PISO | 406.80M2 |
| PLANTA 3° PISO | 372.36M2 |
| PLANTA 4° PISO | 359.28M2 |
| PLANTA 5° PISO | 359.28M2 |
| PLANTA 6° PISO | 359.45M2 |
| PLANTA 7° PISO | 188.91M2 |
| SUP. CUBIERTA TOTAL | 2982.84M2 |

**PLANILLA DE ABERTURAS**

| TIPO | CANT | DIMENSION | | AREAS | | OBSERVACIÓN |
|---|---|---|---|---|---|---|
| | | ANCHO | ALTO | I° | V° | |
| P1 | 1 | 1.50 | 2.50 | 0.49 | 0.24 | DE ABRIR |
| P2 | 1 | 1.60 | 2.07 | ---- | ---- | DE ABRIR |
| P3 | 58 | 0.80 | 2.00 | ---- | ---- | DE ABRIR |
| P4 | 1 | 0.90 | 2.00 | ---- | ---- | VAIVÉN |
| P5 | 86 | 0.90 | 2.00 | ---- | ---- | DE ABRIR |
| P6 | 3 | 1.40 | 2.00 | ---- | ---- | VAIVÉN |
| P7 | 4 | 1.00 | 2.00 | ---- | ---- | DE ABRIR |
| P8 | 59 | 0.70 | 2.00 | ---- | ---- | DE ABRIR |
| P9 | 1 | 1.16 | 2.00 | ---- | ---- | DE ABRIR |
| P10 | 1 | 0.70 | 2.00 | ---- | ---- | CORREDIZA |
| P11 | 1 | 1.20 | 2.00 | ---- | ---- | DE ABRIR |
| P12 | 8 | 1.30 | 2.00 | ---- | ---- | DE ABRIR |
| P13 | 4 | 0.90 | 2.00 | ---- | ---- | CORREDIZA |
| P14 | 2 | 1.80 | 2.00 | ---- | ---- | DE ABRIR |
| P15 | 2 | 1.75 | 2.00 | ---- | ---- | VAIVÉN |
| P16 | 1 | 1.60 | 2.00 | ---- | ---- | DE ABRIR |
| V1 | 105 | 1.20 | 1.20 | 1.44 | 1.44 | DE ABRIR |
| V2 | 2 | 1.60 | 0.37 | 0.59 | ---- | VIDRIO FIJO |
| V3 | 2 | 0.32 | 2.50 | ---- | ---- | VIDRIO FIJO |
| V4 | 1 | 1.98 | 1.00 | ---- | ---- | VIDRIO FIJO |
| V5 | 1 | 1.20 | 1.20 | 1.44 | 0.72 | CORREDIZA |
| V6 | 2 | 0.85 | 1.00 | 0.85 | 0.85 | DE ABRIR |
| V7 | 3 | 2.40 | 1.20 | 1.08 | 1.08 | CORREDIZA |
| V8 | 13 | 0.90 | 1.50 | 1.35 | 1.35 | DE ABRIR |
| V9 | 17 | 1.40 | 1.20 | 1.68 | 1.68 | DE ABRIR |
| V10 | 5 | 1.90 | 1.50 | 2.85 | 2.85 | DE ABRIR |
| V11 | 7 | 0.90 | 1.20 | 1.08 | 1.08 | DE ABRIR |
| V12 | 1 | 3.00 | 1.50 | 4.50 | 2.25 | BANDEROLA |
| V13 | 3 | 0.50 | 0.35 | 0.18 | 0.09 | BANDEROLA |

## CLINICA PRIVADA : "CHUTRO"

| CIRC. | SECC. | MZA. | PARC. |
|---|---|---|---|
| 04 | 02 | 042 | 030 |

RAZON SOCIAL : CLINICA CHUTRO S.R.L.

CALLE: AV.COLON N° 788 - BARRIO: CENTRO - CORDOBA CAPITAL

CROQUIS DE UBICACIÓN

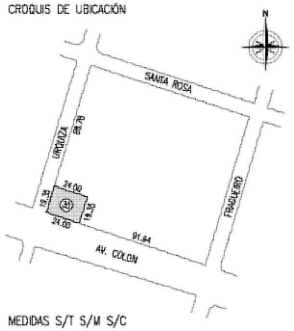


MEDIDAS S/T S/M S/C

TITULAR : BUSTOS RODRIGO

TRANSCRIPCION Y RELEVAMIENTO ACTUALIZADO

Gastón Sentagne
ARQUITECTO
M.P 6723

ARQ. GASTON SENTAGNE
M.P : 1-6723

SUP.DE TERRENO S/T S/C S/M : 464.40

SUP.DE CUB. DE USO ACTIVIDAD: 2982.84

LEGAJO N°

OBSERVACIONES

CONTENIDO : PLANTA CUARTO PISO

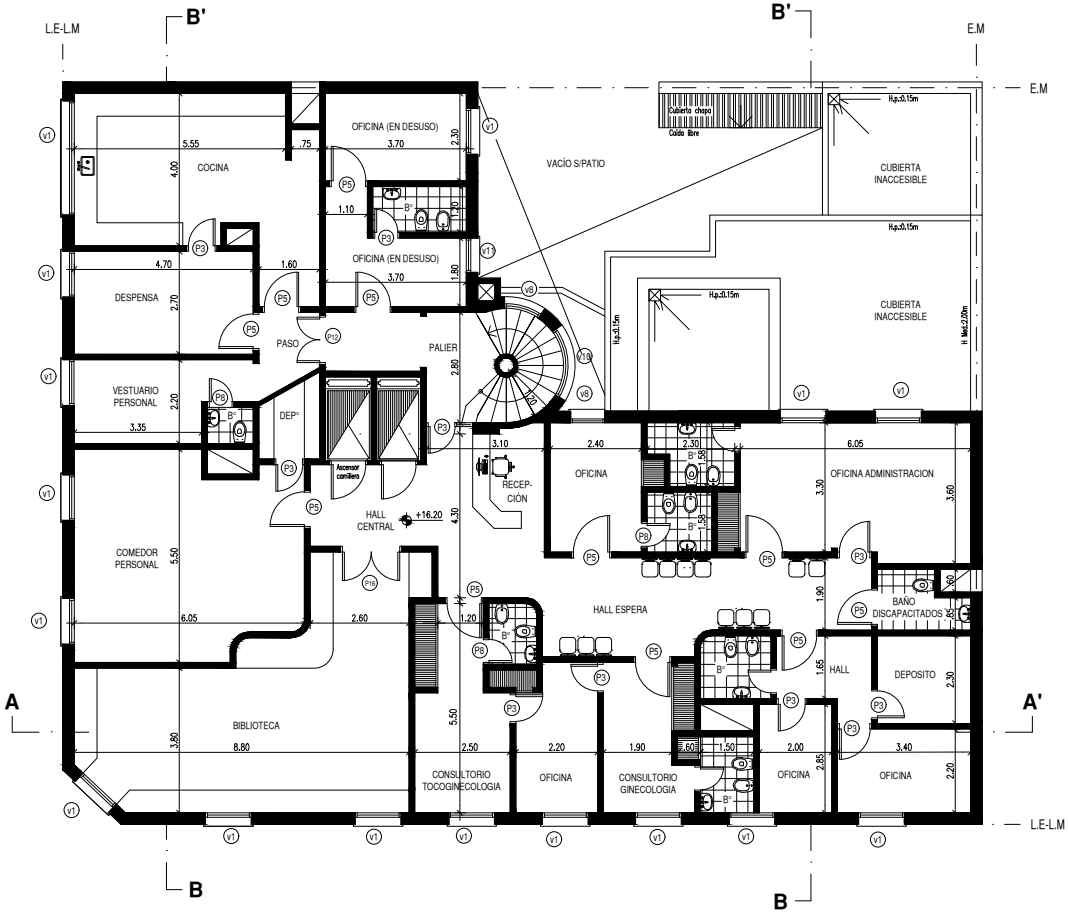


# PLANTA 5° PISO

ESCALA: 1:100

**PLANILLA SUPERFICIES**

| PLANTA PISOS | SUPERFICIE/M2 |
|---|---|
| PLANTA SUBSUELO | 121.23M2 |
| PLANTA BAJA | 421.72M2 |
| PLANTA 1° PISO | 393.79M2 |
| PLANTA 2° PISO | 406.80M2 |
| PLANTA 3° PISO | 372.36M2 |
| PLANTA 4° PISO | 359.28M2 |
| PLANTA 5° PISO | 359.28M2 |
| PLANTA 6° PISO | 359.45M2 |
| PLANTA 7° PISO | 188.91M2 |
| SUP. CUBIERTA TOTAL | 2982.84M2 |

**PLANILLA DE ABERTURAS**

| TIPO | CANT | DIMENSION | | AREAS | | OBSERVACIÓN |
|---|---|---|---|---|---|---|
| | | ANCHO | ALTO | I° | V° | |
| P1 | 1 | 1.50 | 2.50 | 0.49 | 0.24 | DE ABRIR |
| P2 | 1 | 1.60 | 2.07 | ---- | ---- | DE ABRIR |
| P3 | 58 | 0.80 | 2.00 | ---- | ---- | DE ABRIR |
| P4 | 1 | 0.90 | 2.00 | ---- | ---- | VAIVÉN |
| P5 | 86 | 0.90 | 2.00 | ---- | ---- | DE ABRIR |
| P6 | 3 | 1.40 | 2.00 | ---- | ---- | VAIVÉN |
| P7 | 4 | 1.00 | 2.00 | ---- | ---- | DE ABRIR |
| P8 | 59 | 0.70 | 2.00 | ---- | ---- | DE ABRIR |
| P9 | 1 | 1.16 | 2.00 | ---- | ---- | DE ABRIR |
| P10 | 1 | 0.70 | 2.00 | ---- | ---- | CORREDIZA |
| P11 | 1 | 1.20 | 2.00 | ---- | ---- | DE ABRIR |
| P12 | 8 | 1.30 | 2.00 | ---- | ---- | DE ABRIR |
| P13 | 4 | 0.90 | 2.00 | ---- | ---- | CORREDIZA |
| P14 | 2 | 1.80 | 2.00 | ---- | ---- | DE ABRIR |
| P15 | 2 | 1.75 | 2.00 | ---- | ---- | VAIVÉN |
| P16 | 1 | 1.60 | 2.00 | ---- | ---- | DE ABRIR |
| V1 | 105 | 1.20 | 1.20 | 1.44 | 1.44 | DE ABRIR |
| V2 | 2 | 1.60 | 0.37 | 0.59 | ---- | VIDRIO FIJO |
| V3 | 2 | 0.32 | 2.50 | ---- | ---- | VIDRIO FIJO |
| V4 | 1 | 1.98 | 1.00 | ---- | ---- | VIDRIO FIJO |
| V5 | 1 | 1.20 | 1.20 | 1.44 | 0.72 | CORREDIZA |
| V6 | 2 | 0.85 | 1.00 | 0.85 | 0.85 | DE ABRIR |
| V7 | 3 | 2.40 | 1.20 | 1.08 | 1.08 | CORREDIZA |
| V8 | 13 | 0.90 | 1.50 | 1.35 | 1.35 | DE ABRIR |
| V9 | 17 | 1.40 | 1.20 | 1.68 | 1.68 | DE ABRIR |
| V10 | 5 | 1.90 | 1.50 | 2.85 | 2.85 | DE ABRIR |
| V11 | 7 | 0.90 | 1.20 | 1.08 | 1.08 | DE ABRIR |
| V12 | 1 | 3.00 | 1.50 | 4.50 | 2.25 | BANDEROLA |
| V13 | 3 | 0.50 | 0.35 | 0.18 | 0.09 | BANDEROLA |

## CLINICA PRIVADA : "CHUTRO"

| CIRC. | SECC. | MZA. | PARC. |
|---|---|---|---|
| 04 | 02 | 042 | 030 |

RAZON SOCIAL : CLINICA CHUTRO S.R.L.

CALLE: AV.COLON N° 788 - BARRIO: CENTRO - CORDOBA CAPITAL

CROQUIS DE UBICACIÓN

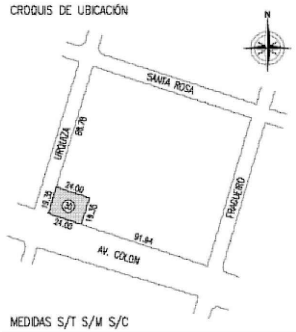


MEDIDAS S/T S/M S/C

SUP.DE TERRENO S/T S/C S/M : 464.40

SUP.DE CUB. DE USO ACTIVIDAD: 2982.84

LEGAJO N°

TITULAR : BUSTOS RODRIGO

TRANSCRIPCION Y RELEVAMIENTO ACTUALIZADO

Gastón Sentagne
ARQUITECTO
M.P. 6723

ARQ. GASTON SENTAGNE
M.P : 1-6723

OBSERVACIONES

CONTENIDO : PLANTA QUINTO PISO

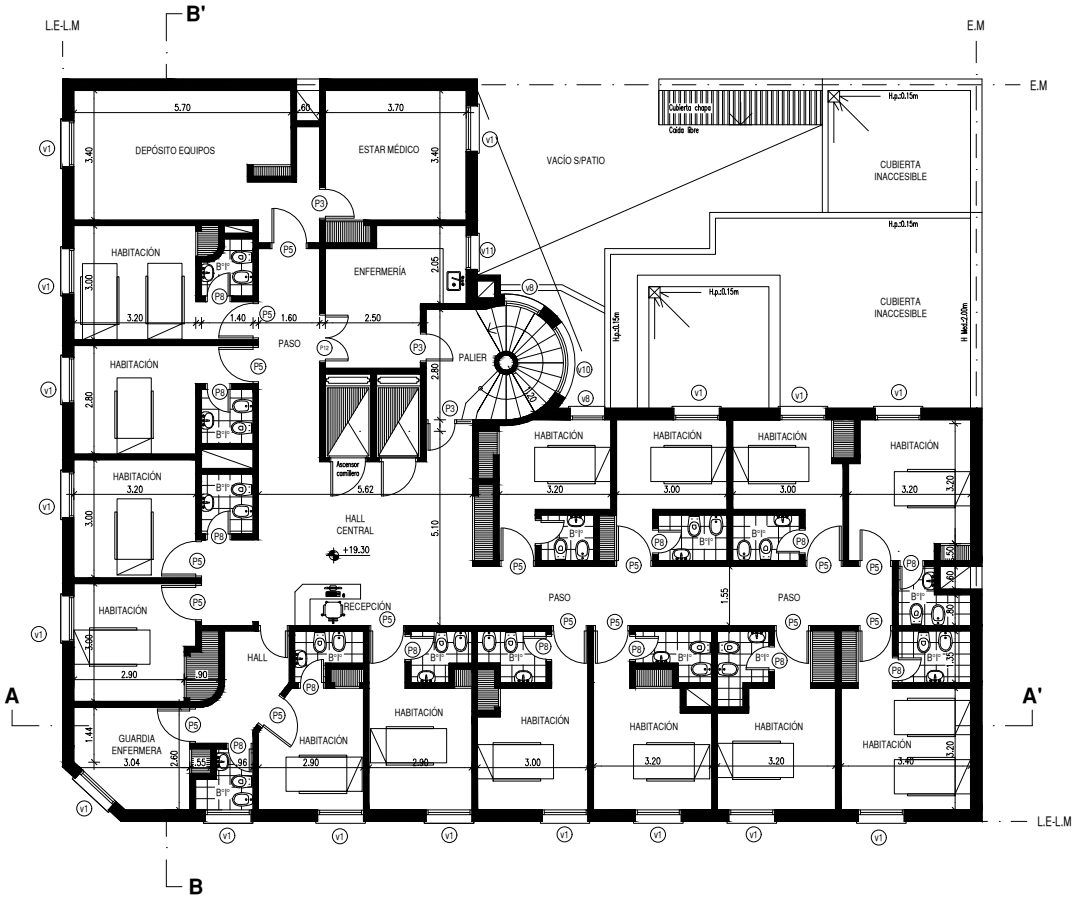


## PLANTA 6° PISO

ESCALA: 1:100

**PLANILLA SUPERFICIES**

| PLANTA PISOS | SUPERFICIE/M2 |
|---|---|
| PLANTA SUBSUELO | 121.23M2 |
| PLANTA BAJA | 421.72M2 |
| PLANTA 1° PISO | 393.79M2 |
| PLANTA 2° PISO | 406.80M2 |
| PLANTA 3° PISO | 372.36M2 |
| PLANTA 4° PISO | 359.28M2 |
| PLANTA 5° PISO | 359.28M2 |
| PLANTA 6° PISO | 359.45M2 |
| PLANTA 7° PISO | 188.91M2 |
| SUP. CUBIERTA TOTAL | 2982.84M2 |

**PLANILLA DE ABERTURAS**

| TIPO | CANT | DIMENSION | | AREAS | | OBSERVACIÓN |
|---|---|---|---|---|---|---|
| | | ANCHO | ALTO | I° | V° | |
| P1 | 1 | 1.50 | 2.50 | 0.49 | 0.24 | DE ABRIR |
| P2 | 1 | 1.60 | 2.07 | ---- | ---- | DE ABRIR |
| P3 | 58 | 0.80 | 2.00 | ---- | ---- | DE ABRIR |
| P4 | 1 | 0.90 | 2.00 | ---- | ---- | VAIVÉN |
| P5 | 86 | 0.90 | 2.00 | ---- | ---- | DE ABRIR |
| P6 | 3 | 1.40 | 2.00 | ---- | ---- | VAIVÉN |
| P7 | 4 | 1.00 | 2.00 | ---- | ---- | DE ABRIR |
| P8 | 59 | 0.70 | 2.00 | ---- | ---- | DE ABRIR |
| P9 | 1 | 1.16 | 2.00 | ---- | ---- | DE ABRIR |
| P10 | 1 | 0.70 | 2.00 | ---- | ---- | CORREDIZA |
| P11 | 1 | 1.20 | 2.00 | ---- | ---- | DE ABRIR |
| P12 | 8 | 1.30 | 2.00 | ---- | ---- | DE ABRIR |
| P13 | 4 | 0.90 | 2.00 | ---- | ---- | CORREDIZA |
| P14 | 2 | 1.80 | 2.00 | ---- | ---- | DE ABRIR |
| P15 | 2 | 1.75 | 2.00 | ---- | ---- | VAIVÉN |
| P16 | 1 | 1.60 | 2.00 | ---- | ---- | DE ABRIR |
| V1 | 105 | 1.20 | 1.20 | 1.44 | 1.44 | DE ABRIR |
| V2 | 2 | 1.60 | 0.37 | 0.59 | ---- | VIDRIO FIJO |
| V3 | 2 | 0.32 | 2.50 | ---- | ---- | VIDRIO FIJO |
| V4 | 1 | 1.98 | 1.00 | ---- | ---- | VIDRIO FIJO |
| V5 | 1 | 1.20 | 1.20 | 1.44 | 0.72 | CORREDIZA |
| V6 | 2 | 0.85 | 1.00 | 0.85 | 0.85 | DE ABRIR |
| V7 | 3 | 2.40 | 1.20 | 1.08 | 1.08 | CORREDIZA |
| V8 | 13 | 0.90 | 1.50 | 1.35 | 1.35 | DE ABRIR |
| V9 | 17 | 1.40 | 1.20 | 1.68 | 1.68 | DE ABRIR |
| V10 | 5 | 1.90 | 1.50 | 2.85 | 2.85 | DE ABRIR |
| V11 | 7 | 0.90 | 1.20 | 1.08 | 1.08 | DE ABRIR |
| V12 | 1 | 3.00 | 1.50 | 4.50 | 2.25 | BANDEROLA |
| V13 | 3 | 0.50 | 0.35 | 0.18 | 0.09 | BANDEROLA |

# CLINICA PRIVADA : "CHUTRO"

| CIRC. | SECC. | MZA. | PARC. |
|---|---|---|---|
| 04 | 02 | 042 | 030 |

RAZON SOCIAL : CLINICA CHUTRO S.R.L.

CALLE: AV.COLON N° 788 - BARRIO: CENTRO - CORDOBA CAPITAL

CROQUIS DE UBICACIÓN

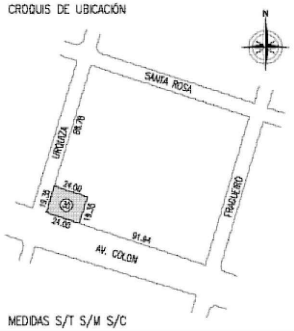


TITULAR : BUSTOS RODRIGO

TRANSCRIPCION Y RELEVAMIENTO ACTUALIZADO

Gastón Sentagne
ARQUITECTO
M.P. 6723

ARQ. GASTON SENTAGNE
M.P : 1-6723

SUP.DE TERRENO S/T S/C S/M : 464.40

SUP.DE CUB. DE USO ACTIVIDAD: 2982.84

LEGAJO N°

OBSERVACIONES

CONTENIDO :SEXTO PISO

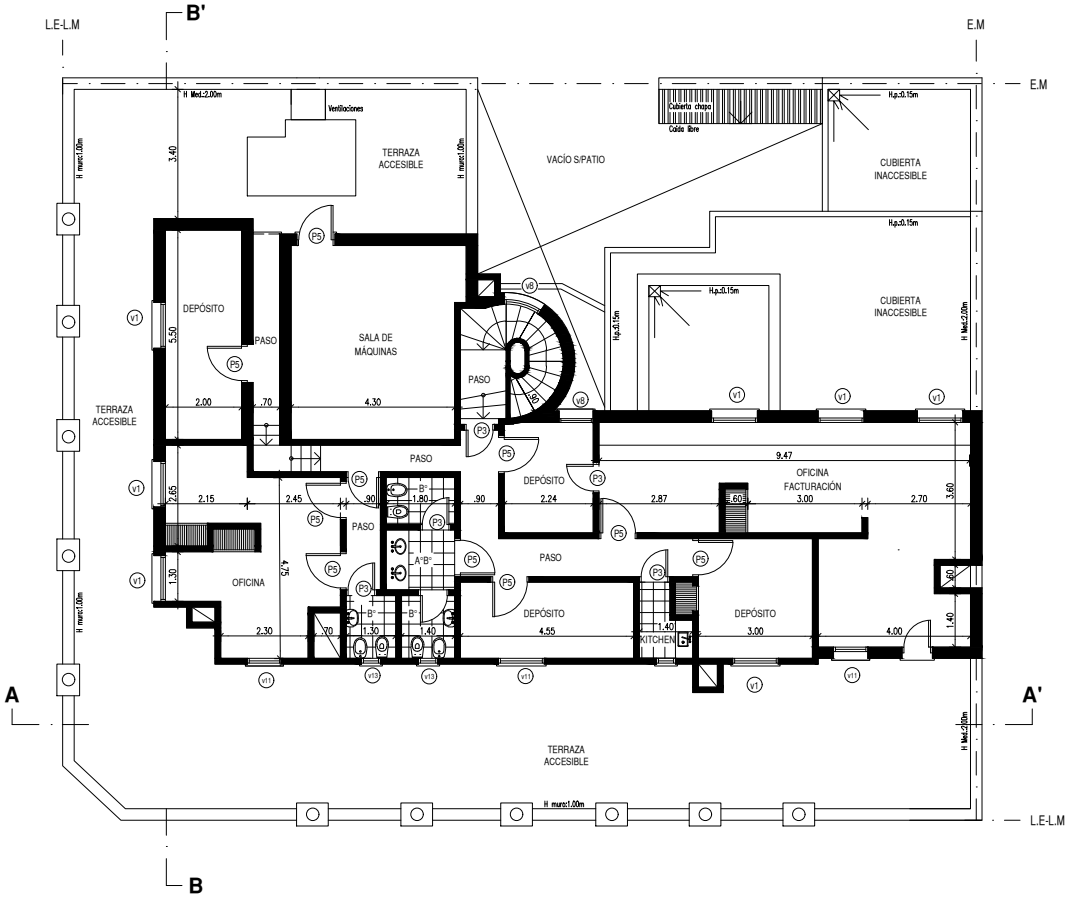


# PLANTA 7° PISO

ESCALA: 1:100

**PLANILLA SUPERFICIES**

| PLANTA PISOS | SUPERFICIE/M2 |
|---|---|
| PLANTA SUBSUELO | 121.23M2 |
| PLANTA BAJA | 421.72M2 |
| PLANTA 1° PISO | 393.79M2 |
| PLANTA 2° PISO | 406.80M2 |
| PLANTA 3° PISO | 372.36M2 |
| PLANTA 4° PISO | 359.28M2 |
| PLANTA 5° PISO | 359.28M2 |
| PLANTA 6° PISO | 359.45M2 |
| PLANTA 7° PISO | 188.91M2 |
| SUP. CUBIERTA TOTAL | 2982.84M2 |

**PLANILLA DE ABERTURAS**

| TIPO | CANT | DIMENSION | | AREAS | | OBSERVACIÓN |
|---|---|---|---|---|---|---|
| | | ANCHO | ALTO | I° | V° | |
| P1 | 1 | 1.50 | 2.50 | 0.49 | 0.24 | DE ABRIR |
| P2 | 1 | 1.60 | 2.07 | ---- | ---- | DE ABRIR |
| P3 | 58 | 0.80 | 2.00 | ---- | ---- | DE ABRIR |
| P4 | 1 | 0.90 | 2.00 | ---- | ---- | VAIVÉN |
| P5 | 86 | 0.90 | 2.00 | ---- | ---- | DE ABRIR |
| P6 | 3 | 1.40 | 2.00 | ---- | ---- | VAIVÉN |
| P7 | 4 | 1.00 | 2.00 | ---- | ---- | DE ABRIR |
| P8 | 59 | 0.70 | 2.00 | ---- | ---- | DE ABRIR |
| P9 | 1 | 1.16 | 2.00 | ---- | ---- | DE ABRIR |
| P10 | 1 | 0.70 | 2.00 | ---- | ---- | CORREDIZA |
| P11 | 1 | 1.20 | 2.00 | ---- | ---- | DE ABRIR |
| P12 | 8 | 1.30 | 2.00 | ---- | ---- | DE ABRIR |
| P13 | 4 | 0.90 | 2.00 | ---- | ---- | CORREDIZA |
| P14 | 2 | 1.80 | 2.00 | ---- | ---- | DE ABRIR |
| P15 | 2 | 1.75 | 2.00 | ---- | ---- | VAIVÉN |
| P16 | 1 | 1.60 | 2.00 | ---- | ---- | DE ABRIR |
| V1 | 105 | 1.20 | 1.20 | 1.44 | 1.44 | DE ABRIR |
| V2 | 2 | 1.60 | 0.37 | 0.59 | ---- | VIDRIO FIJO |
| V3 | 2 | 0.32 | 2.50 | ---- | ---- | VIDRIO FIJO |
| V4 | 1 | 1.98 | 1.00 | ---- | ---- | VIDRIO FIJO |
| V5 | 1 | 1.20 | 1.20 | 1.44 | 0.72 | CORREDIZA |
| V6 | 2 | 0.85 | 1.00 | 0.85 | 0.85 | DE ABRIR |
| V7 | 3 | 2.40 | 1.20 | 1.08 | 1.08 | CORREDIZA |
| V8 | 13 | 0.90 | 1.50 | 1.35 | 1.35 | DE ABRIR |
| V9 | 17 | 1.40 | 1.20 | 1.68 | 1.68 | DE ABRIR |
| V10 | 5 | 1.90 | 1.50 | 2.85 | 2.85 | DE ABRIR |
| V11 | 7 | 0.90 | 1.20 | 1.08 | 1.08 | DE ABRIR |
| V12 | 1 | 3.00 | 1.50 | 4.50 | 2.25 | BANDEROLA |
| V13 | 3 | 0.50 | 0.35 | 0.18 | 0.09 | BANDEROLA |

## CLINICA PRIVADA : "CHUTRO"

| CIRC. | SECC. | MZA. | PARC. |
|---|---|---|---|
| 04 | 02 | 042 | 030 |

RAZON SOCIAL : CLINICA CHUTRO S.R.L.

CALLE: AV.COLON N° 788 - BARRIO: CENTRO - CORDOBA CAPITAL

CROQUIS DE UBICACIÓN

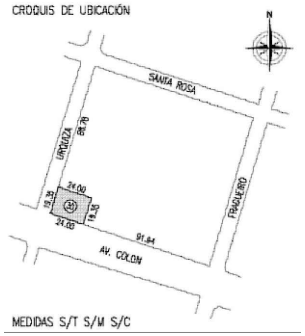


MEDIDAS S/T S/M S/C

TITULAR : BUSTOS RODRIGO

TRANSCRIPCION Y RELEVAMIENTO ACTUALIZADO

Gastón Sentagne
ARQUITECTO
M.P. 6723

ARQ. GASTON SENTAGNE
M.P : 1-6723

SUP.DE TERRENO S/T S/C S/M : 464.40

SUP.DE CUB. DE USO ACTIVIDAD: 2982.84

LEGAJO N°

OBSERVACIONES

CONTENIDO :SEPTIMO PISO